D01 / Ceiling isolation

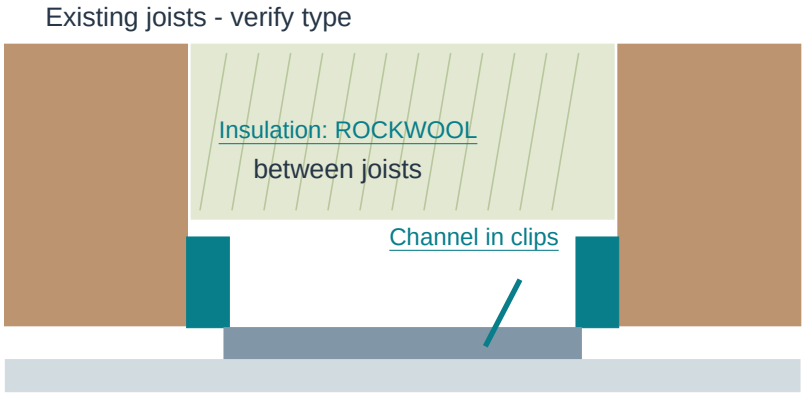

Gypsum screwed to channel

RSIC-1 Low Profile guide (2014)

Joist > clip > channel > gypsum

PAC download index - verify current guide

D02 / Wall-top isolation

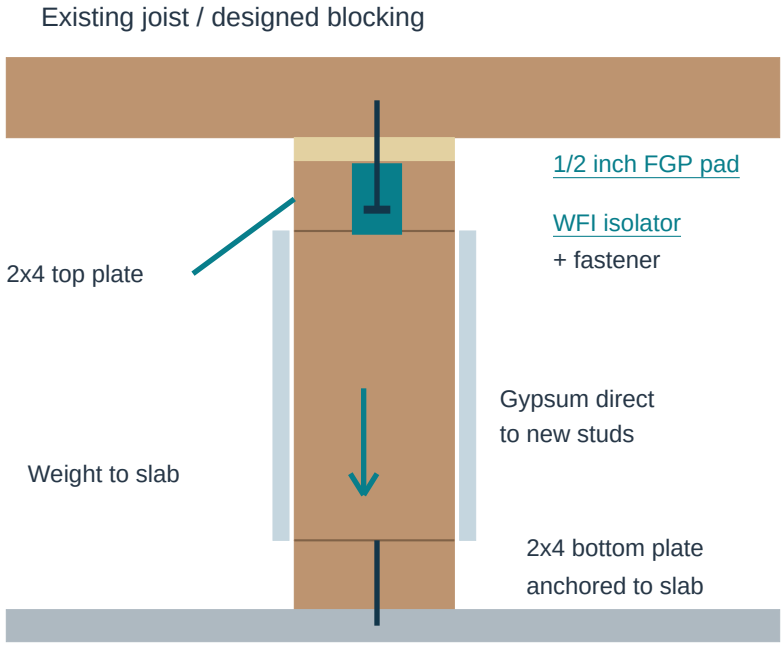

Acoustic perimeter sealant (product example)

D03 / Girder at hallway wall - blocking parallel to girder, between joists.

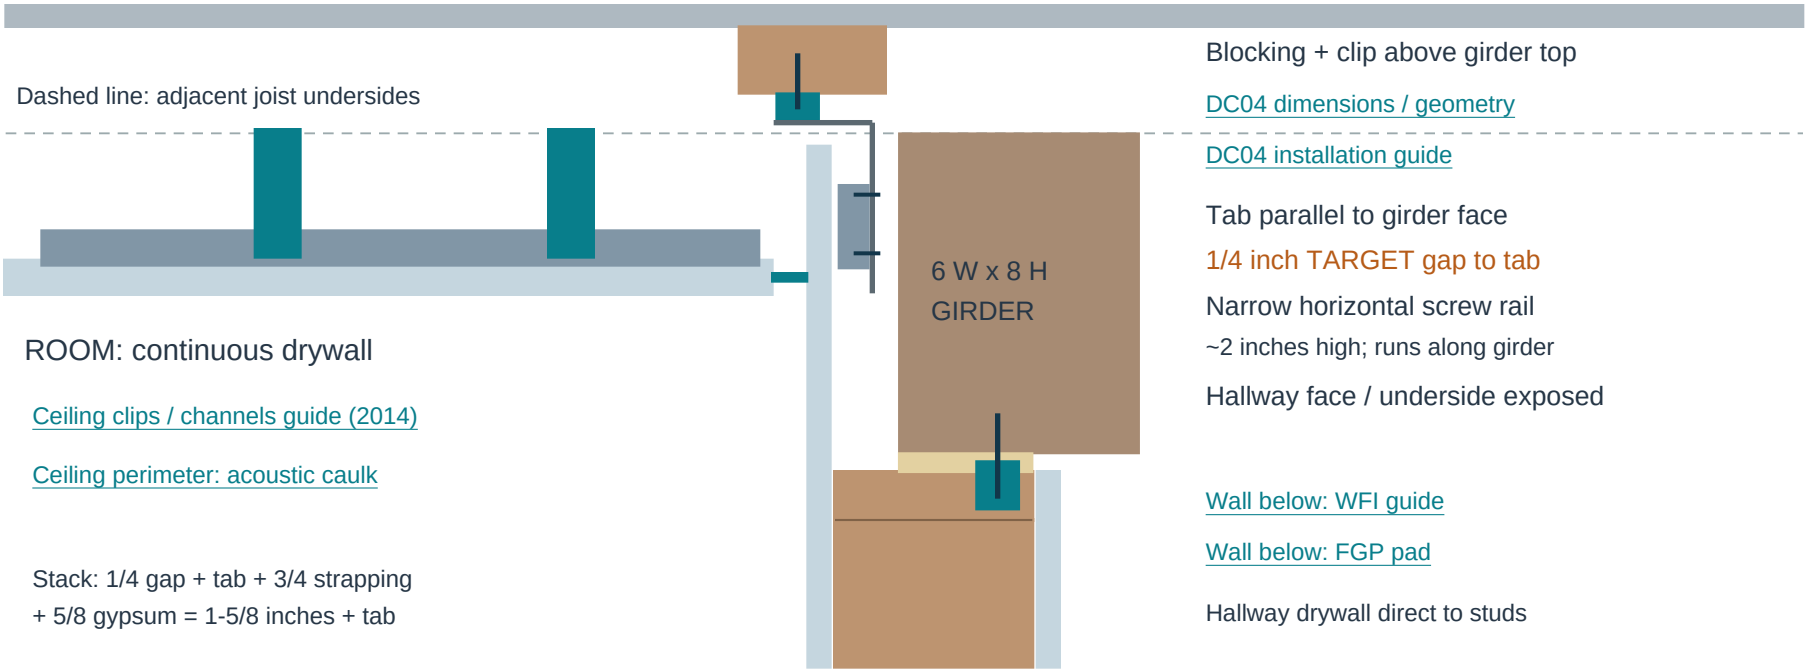

D04 / Two wood doorways beneath girder - no horizontal framing or head jamb

Elevation - looking at door

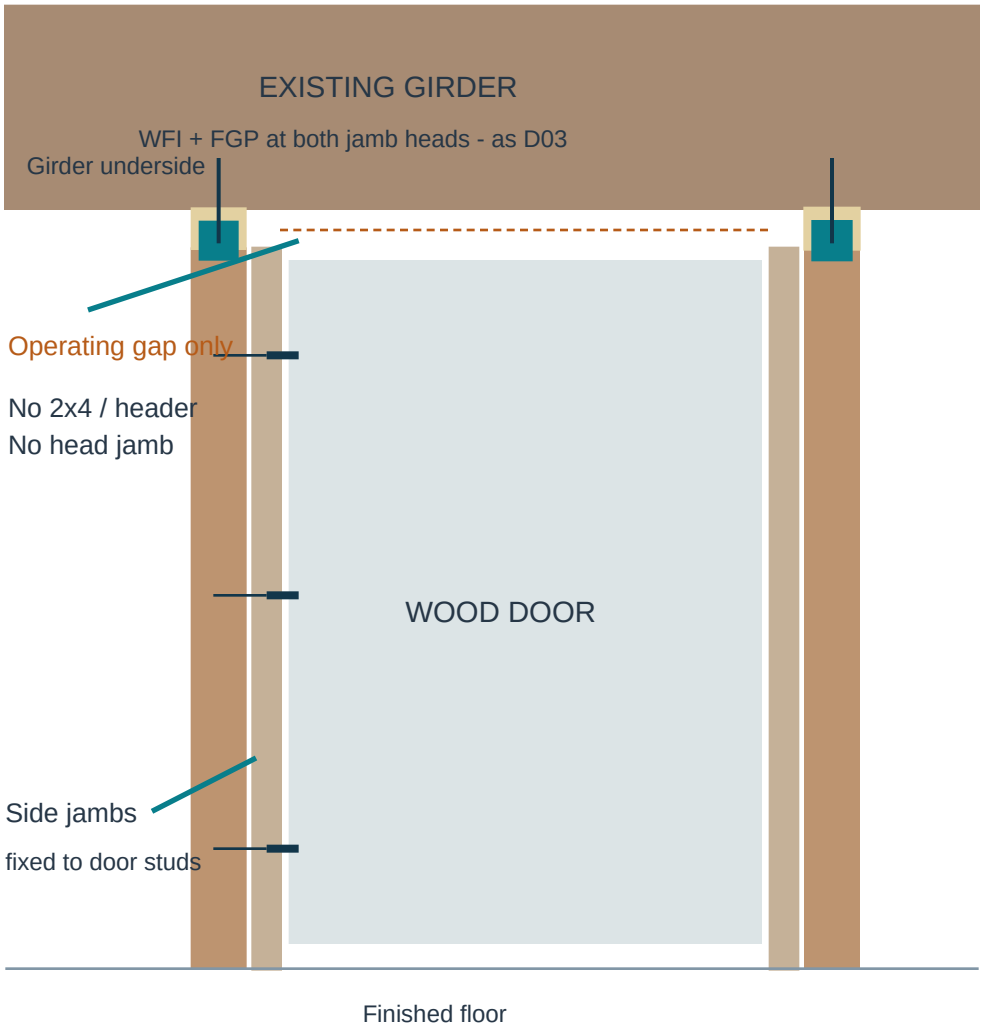

Head section - across girder

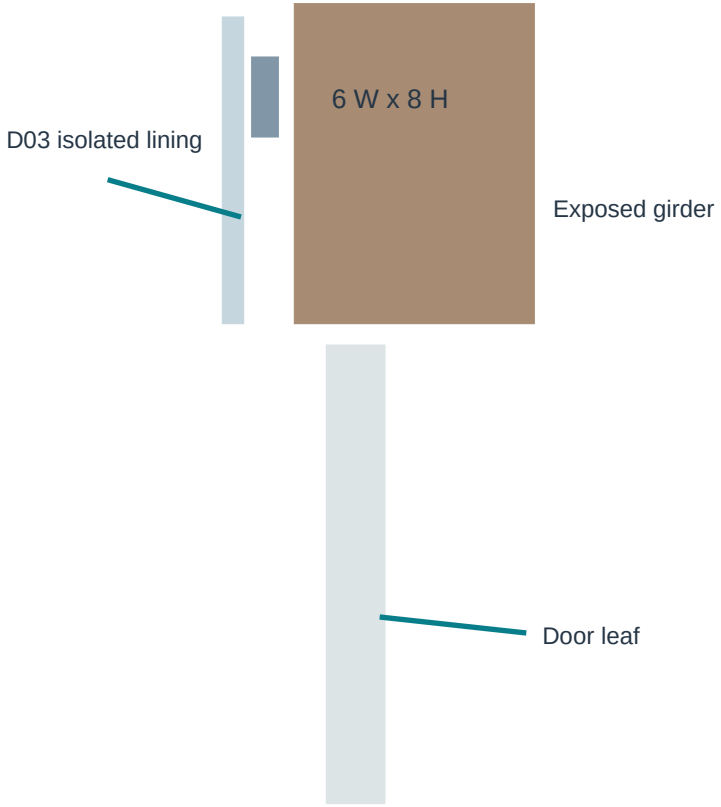

D03 lining - DC04 instructions

Proposed jamb-head connection - WFI guide

FGP pad - manufacturer page

D05 / Rec-room separation wall

Typical section at the interior partition

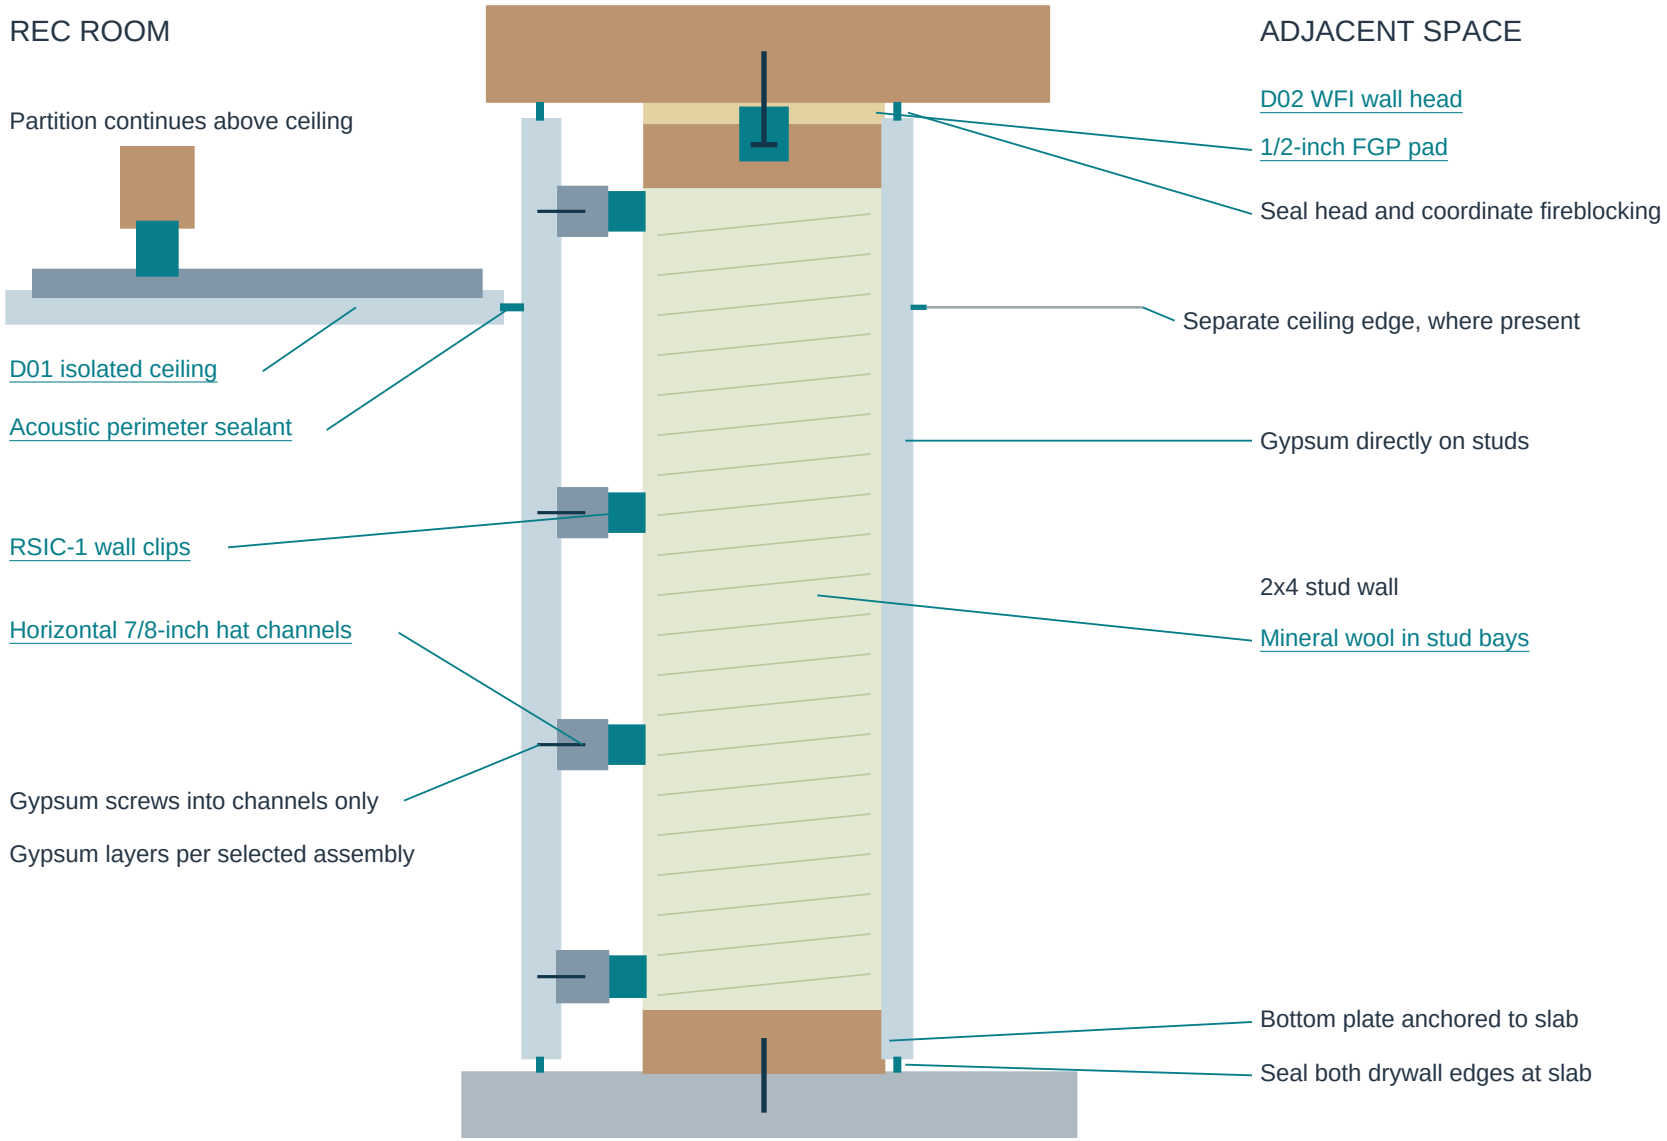

PAC wall installation guide

Coordinate openings, door seals and penetrations with the partition assembly.