139 E 8th STREET BROOKLYN, NY 11218

BASEMENT RENOVATION

LEGEND

- EXISTING WALL/PARTITION TO BE DEMOLISHED
- EXISTING EXTERIOR WALL/PARTITION TO REMAIN
- NEW INTERIOR PARTITION, SEE DETAILS
- EXISTING STEEL COLUMN TO REMAIN
- EXISTING STEEL COLUMN WITH GWB ENCLOSURE
- POWER OUTLET

SYMBOLS

- E. W x H — EXISTING WINDOW TO REMAIN
- W" x H" — NEW WINDOW
- EXISTING DOOR TO REMAIN
- W" x H" — NEW DOOR
- CMD/ SD — CARBON MONOXIDE / SMOKE DETECTOR (HARDWIRED AS PER CODE)
- CFM — TOILET & KITCHEN MECH VENTILATOR
- (E.) — DENOTES EXISTING

BUILDING INFORMATION

BLOCK: 5331
LOT: 97
ZONING DISTRICT: R5
SPECIAL PURPOSE DISTRICT: OCEAN PARKWAY
MAP NUMBER: 22c

LIST OF DRAWINGS

1	T-100.00	TITLE PAGE BUILDING INFORMATION LEGENDS
2	A-100.00	BASEMENT DEMOLITION PLAN
3	A-101.00	PROPOSED BASEMENT PLAN
4	A-102.00	PROPOSED LIGHTING PLAN
5	A-103.00	SECTIONS
6	A-104.00	TYPICAL DETAILS

NOT FOR CONSTRUCTION

Jeff Balinnang Architect
3060 N Jerusalem Rd.
Wantagh, NY 11793
email: info@jbalarch.com
Tel: 934-234-0287

Date Issued: 29 October 2026

Revisions

No.	Date	Issued For

Project Name: BASEMENT RENOVATION

139 E 8th STREET
BROOKLYN, NY 11218


Project Owner: RYAN SIMMS

Sheet Content: TITLE PAGE, BUILDING INFORMATION, LEGENDS

Drawn by:	Scale:
JAB	1/4" = 1'-0"
Checked by:	**Proj. No.**
JAB	2026-05

Sheet: T-100.00

1 OF 6

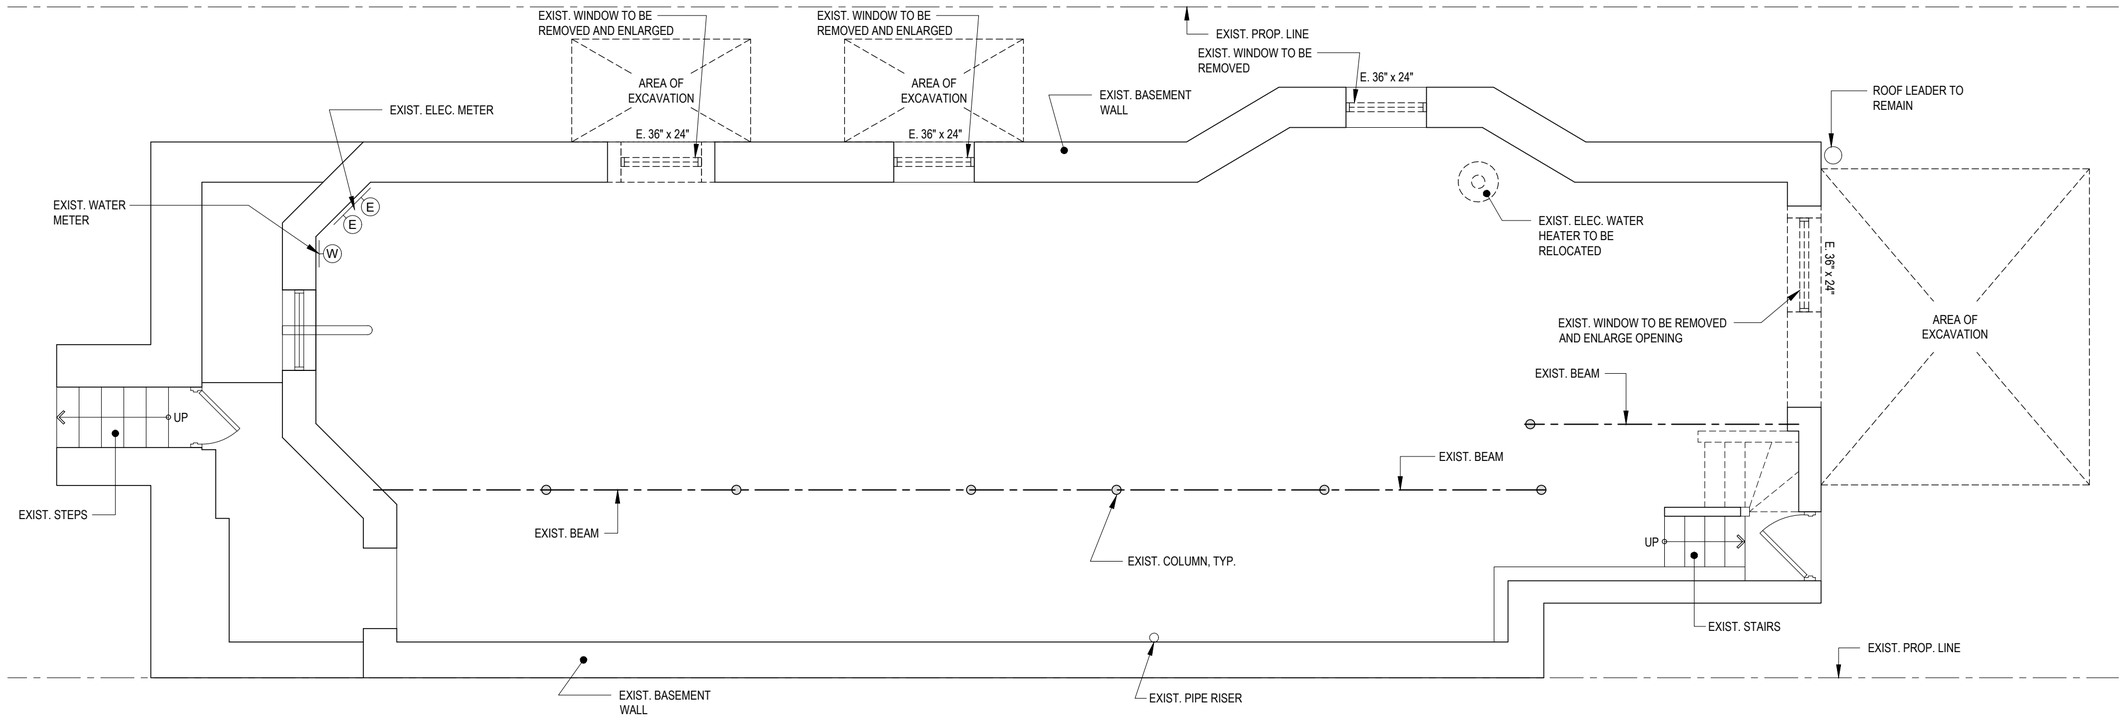

1 BASEMENT DEMOLITION PLAN
SCALE 1/4" = 1'-0"

NOT FOR CONSTRUCTION

Jeff Balinnang Architect

3060 N Jerusalem Rd.
Wantagh, NY 11793
email: info@jbalarch.com
Tel: 934-234-0287

Date Issued:
29 October 2026

Revisions

No.	Date	Issued For

Project Name:
BASEMENT RENOVATION


139 E 8th STREET
BROOKLYN, NY 11218

Project Owner:
RYAN SIMMS

Sheet Content:
DEMOLITION PLAN

Drawn by:	Scale:
JAB	1/4" = 1'-0"
Checked by:	Proj. No.
JAB	2026-05

Sheet:
A-100.00
2 OF 6

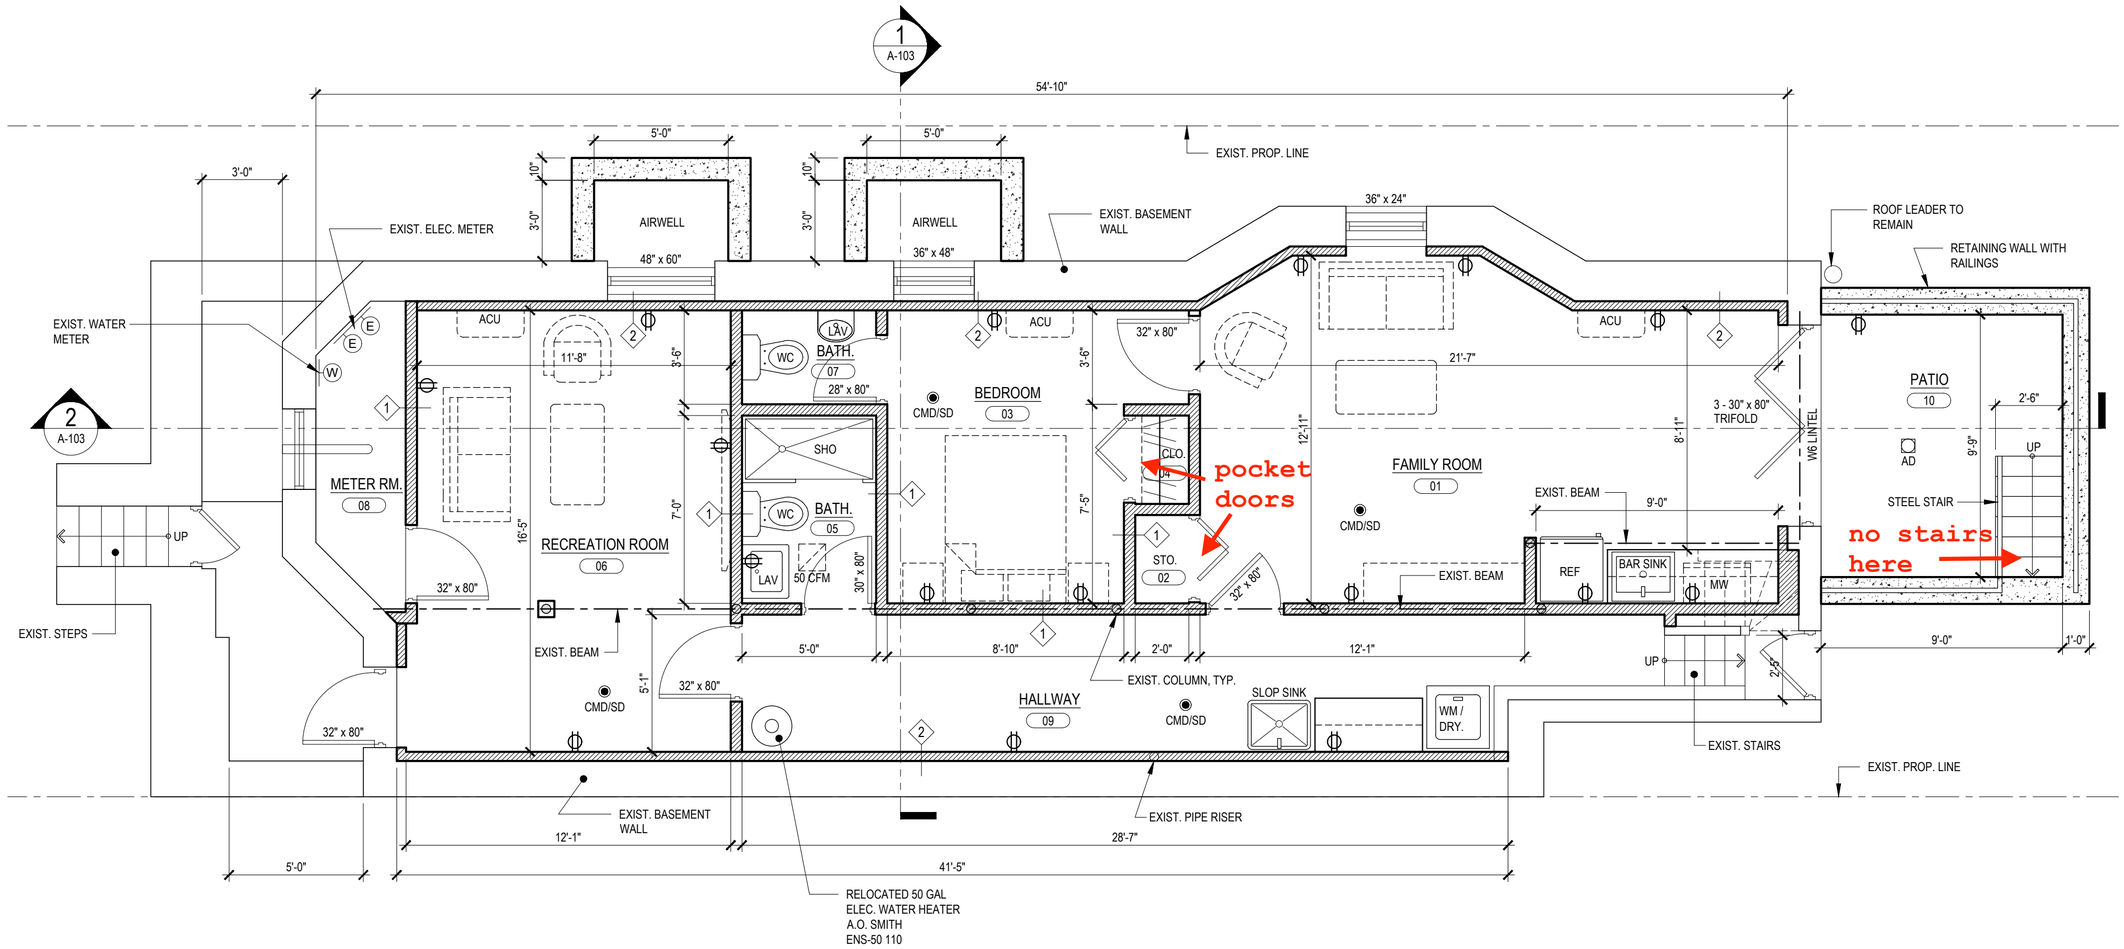

1 PROPOSED BASEMENT PLAN

SCALE 1/4" = 1'-0"

NOT FOR CONSTRUCTION

Jeff Balinnang Architect

3060 N Jerusalem Rd.
Wantagh, NY 11793
email: info@jbalarch.com
Tel: 934-234-0287

Date Issued:
29 October 2026

Revisions

No.	Date	Issued For

Project Name:
BASEMENT RENOVATION


139 E 8th STREET
BROOKLYN, NY 11218

Project Owner:
RYAN SIMMS

Sheet Content:
CONSTRUCTION PLAN

Drawn by:	Scale:
JAB	1/4" = 1'-0"
Checked by:	Proj. No.
JAB	2026-05

Sheet:
A-101.00
3 OF 6

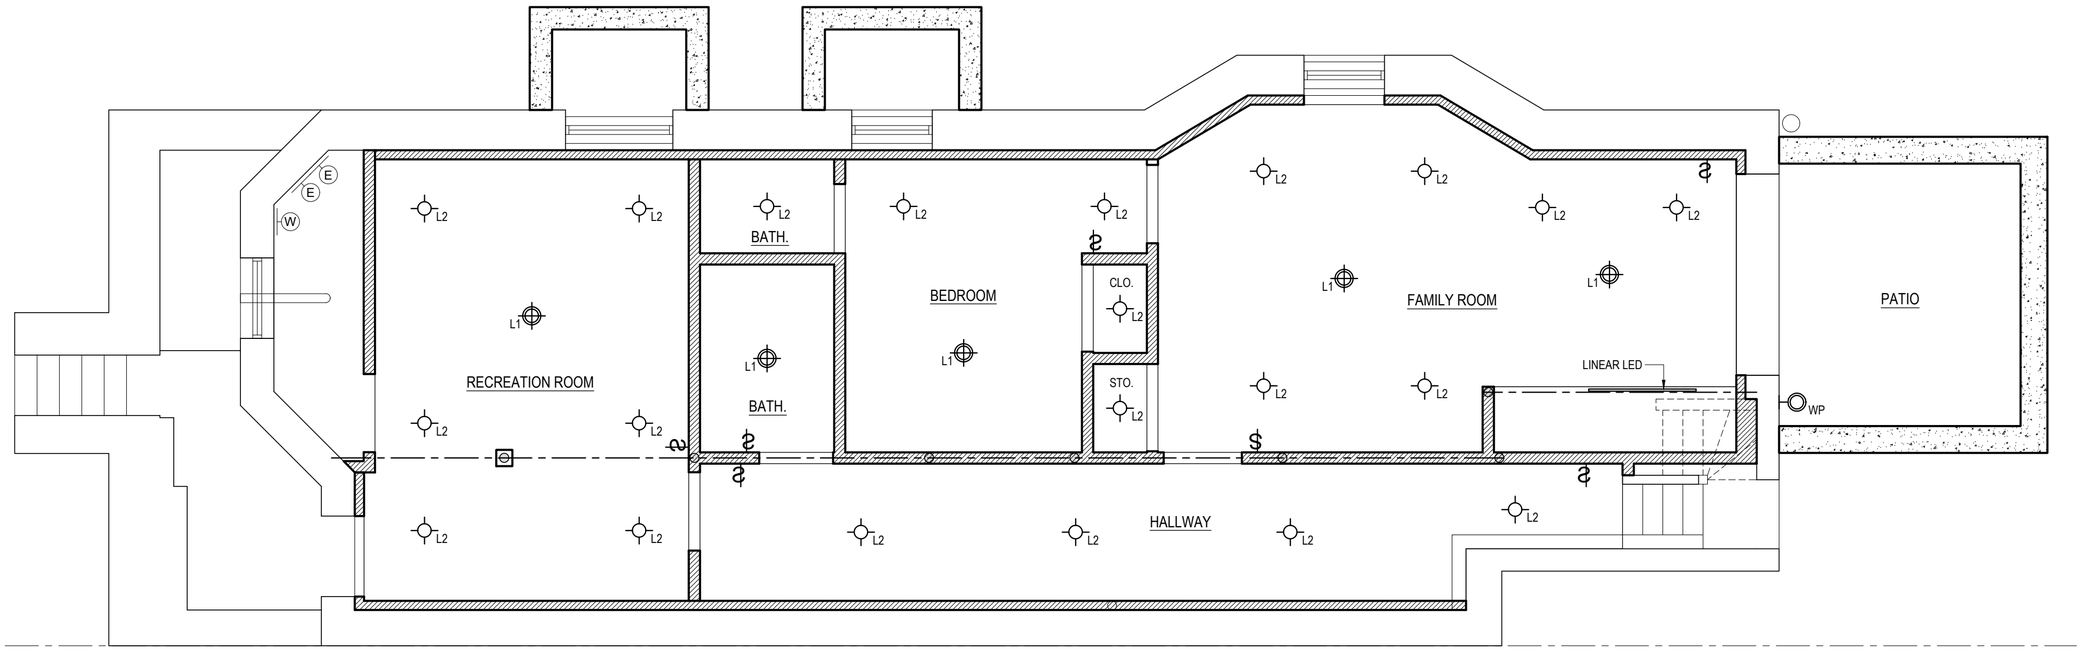

1 PROPOSED LIGHTING PLAN
SCALE 1/4" = 1'-0"

LIGHTING LEGEND

L1	SURFACE MOUNTED CEILING LIGHT FIXTURE
L2	RECESSED MOUNTED CEILING LIGHT FIXTURE
WP	WALL MOUNTED EXTERIOR LIGHT FIXTURE
$	SWITCH

NOT FOR CONSTRUCTION

Jeff Balinnang Architect
3060 N Jerusalem Rd.
Wantagh, NY 11793
email: info@jbalarch.com
Tel: 934-234-0287

Date Issued:
29 October 2026

Revisions

No.	Date	Issued For

Project Name:
BASEMENT RENOVATION


139 E 8th STREET
BROOKLYN, NY 11218

Project Owner:
RYAN SIMMS


Sheet Content:
LIGHTING PLAN

Drawn by:	Scale:
JAB	1/4" = 1'-0"
Checked by:	Proj. No.
JAB	2026-05

Sheet:
A-102.00
4 OF 6

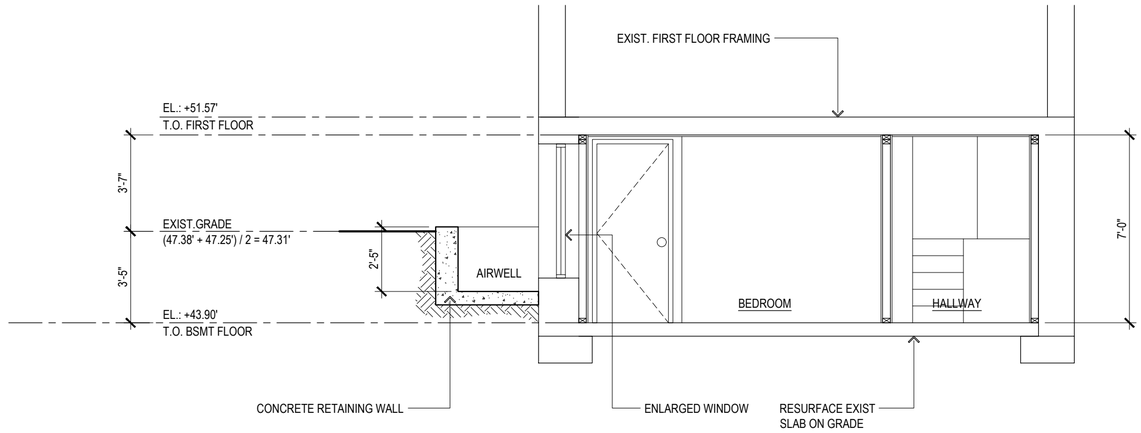

1 CROSS SECTION
SCALE 1/4" = 1'-0"

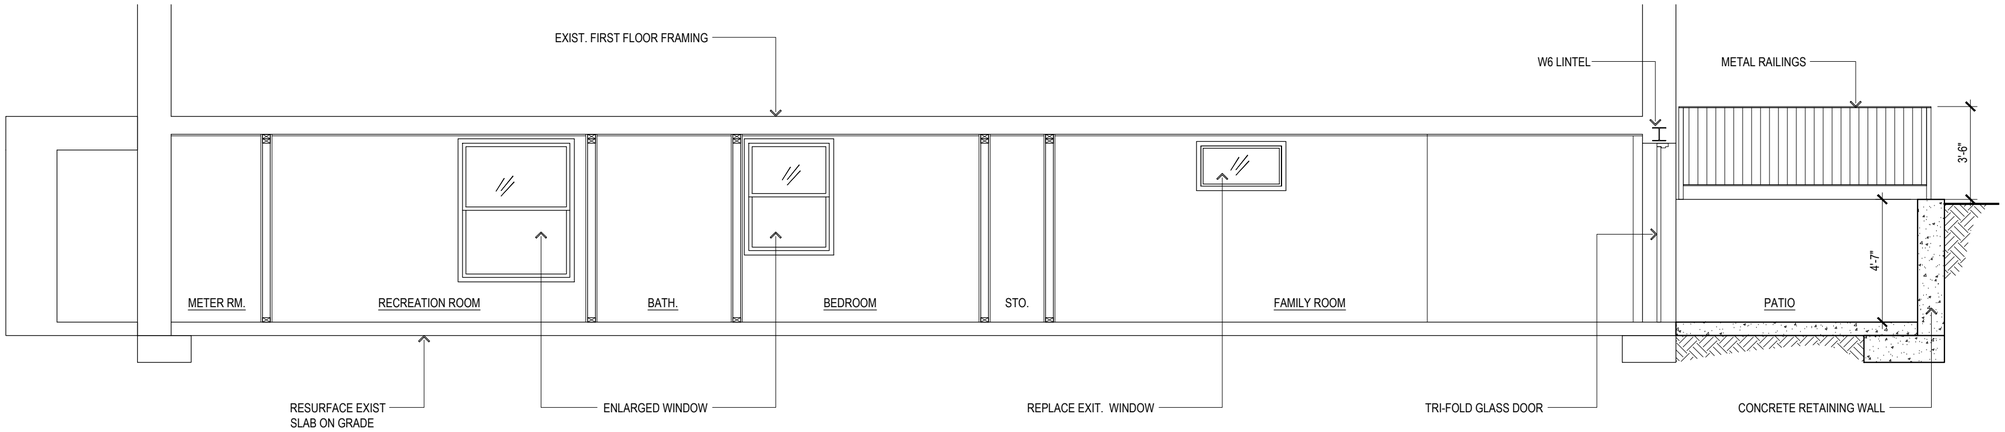

2 LONGITUDINAL SECTION
SCALE 1/4" = 1'-0"

NOT FOR CONSTRUCTION

Jeff Balinnang Architect

3060 N Jerusalem Rd.
Wantagh, NY 11793
email: info@jbalarch.com
Tel: 934-234-0287

Date Issued:
29 October 2026

Revisions

No.	Date	Issued For

Project Name:
BASEMENT RENOVATION

139 E 8th STREET
BROOKLYN, NY 11218

Project Owner:
RYAN SIMMS


Sheet Content:
SECTIONS

Drawn by:	Scale:
JAB	1/4" = 1'-0"
Checked by:	**Proj. No.**
JAB	2026-05

Sheet:
A-103.00
5 OF 6

ROOM FINISH SCHEDULE


RM. NO.	SPACE	WALL	FLOOR	CEILING	MOLDING		REMARKS
					BASE	CEILING	
01	FAMILY ROOM	PAINTED GYPSUM BD.	VINYL TILE	PAINTED GYPSUM BD.	WOOD	WOOD	FLOOR: LEVEL EXISTING CONCRETE SLAB WALLS & CEILING: PRIME AND 2 COATS OF PAINT.
02	STORAGE	PAINTED GYPSUM BD.	VINYL TILE	PAINTED GYPSUM BD.	WOOD	NONE	
03	BEDROOM	PAINTED GYPSUM BD.	VINYL TILE	PAINTED GYPSUM BD.	WOOD	WOOD	
04	CLOSET	PAINTED GYPSUM BD.	VINYL TILE	PAINTED GYPSUM BD.	WOOD	NONE	
05	BATHROOM	PAINTED GYPSUM BD. & CERAMIC WALL TILES	CERAMIC TILE	PAINTED GYPSUM BD.	TILE	NONE	
06	RECREATION ROOM	PAINTED GYPSUM BD.	VINYL TILE	PAINTED GYPSUM BD.	WOOD	WOOD	
07	BATHROOM	PAINTED GYPSUM BD. & CERAMIC WALL TILES	CERAMIC TILE	PAINTED GYPSUM BD.	TILE	NONE	
08	METER ROOM	EXPOSED FOUNDATION WALL	NONE	NONE	NONE	NONE	
09	HALLWAY	PAINTED GYPSUM BD.	CERAMIC TILE	PAINTED GYPSUM BD.	TILE	WOOD	
10	PATIO	PAINTED CONCRETE	CONCRETE TILE	NONE	NONE	NONE	

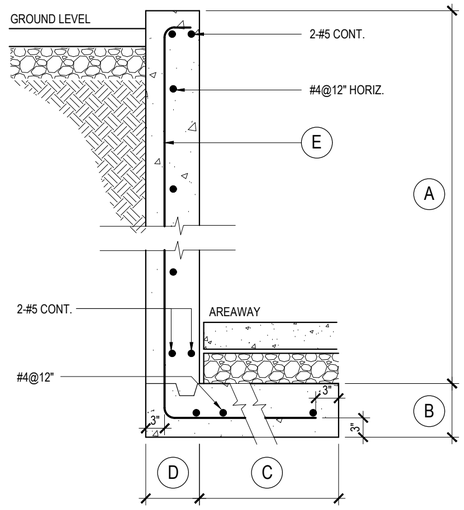


REINFORCEMENT SCHEDULE

A	B	C	D	E
TO 4'-0"	1'-0"	3'-0"	0'-10"	#4@12"O.C.
TO 8'-0"	1'-0"	4'-0"	1'-0"	#5@12"O.C.

1 CONCRETE WALL DETAIL
SCALE 1/2" = 1'-0

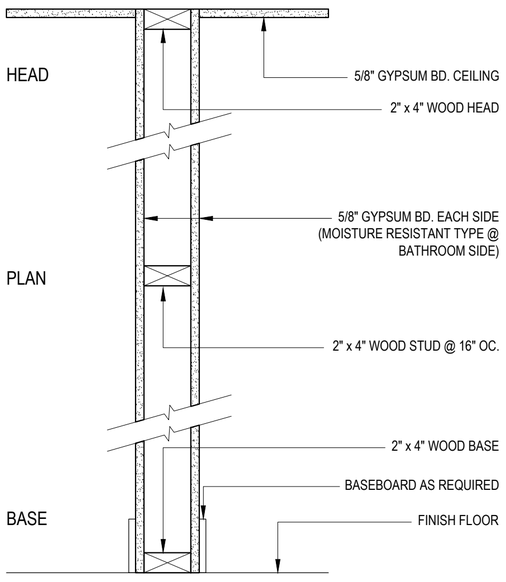

1 UNRATED GWB PARTITION
SCALE: 1 1/2" = 1'-0

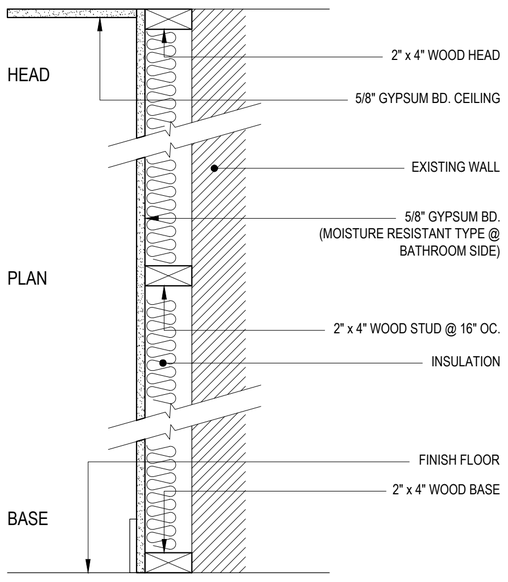

2 FURRED GYP. BD. FINISH
SCALE: 1 1/2" = 1'-0

NOT FOR CONSTRUCTION

Jeff Balinnang Architect

3060 N Jerusalem Rd.
Wantagh, NY 11793
email: info@jbalarch.com
Tel: 934-234-0287

Date Issued:
29 October 2026

Revisions

No.	Date	Issued For

Project Name:
BASEMENT RENOVATION

139 E 8th STREET
BROOKLYN, NY 11218

Project Owner:
RYAN SIMMS

Sheet Content:
TYPICAL DETAILS

Drawn by:	Scale:
JAB	1/4" = 1'-0"
Checked by:	**Proj. No.**
JAB	2026-05

Sheet:
A-104.00
6 OF 6